


Bordure maison

BASE DE CONTROLE - Releve independant, non raccorde au site

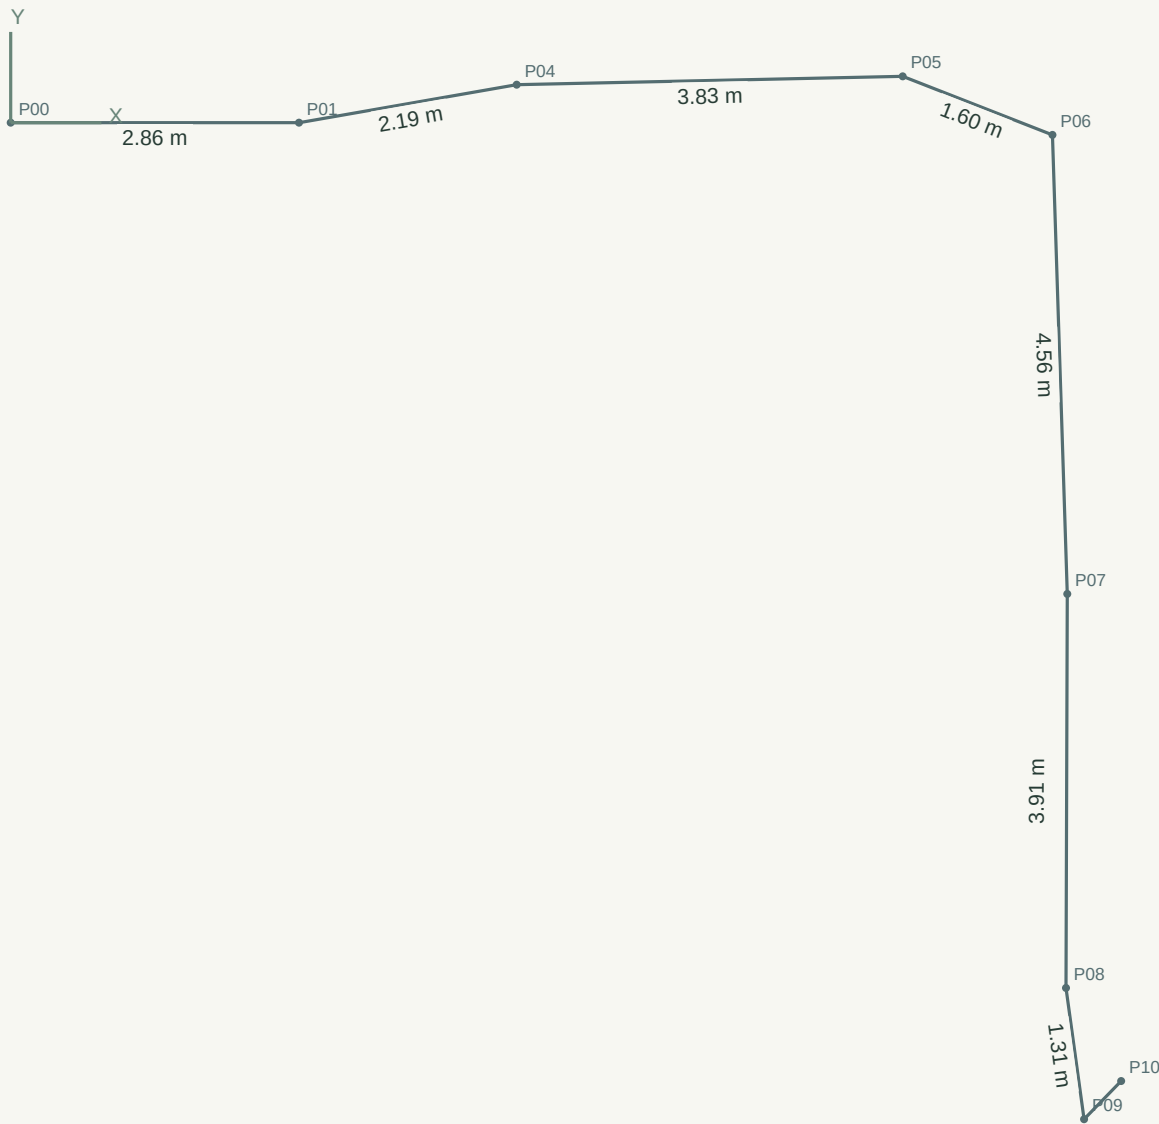

DONNEES LOCALES

Unites : metres | Geometrie : 1:1

Parcours XY : 20.78 m

Trace ouvert : aucune aire affectee

Z local : -0.59 a +0.00 m

Origine : P00 du PDF, non localisee sur site

Nord non documente

Cote	XY (m)	Z debut / fin (m)
C01	2.86	+0.00 / -0.09
C02	0.00	-0.09 / -0.09
C03	0.00	-0.09 / -0.09
C04	2.19	-0.09 / -0.22
C05	3.83	-0.22 / -0.40
C06	1.60	-0.40 / -0.46
C07	4.56	-0.46 / -0.50
C08	3.91	-0.50 / -0.59
C09	1.31	-0.59 / -0.27
C10	0.53	-0.27 / -0.34

XY deduits du trace vectoriel calibre.

Z cotes dans le PDF, arrondis au cm.

Aucun assemblage physique valide.

1 metre



A3 paysage - 1:75 a 100 %, sans adaptation a la page

Source : Bordure maison.pdf, p.1-2. Tableau : valeurs publiees. Dessin : reconstruction vectorielle.

Ce document est une base partielle de restitution, pas un plan d implantation, de propriete ou d execution.

Terrasse de droite

BASE DE CONTROLE - Releve independant, non raccorde au site

DONNEES LOCALES

Unites : metres | Geometrie : 1:1

Parcours XY : 34.49 m

Aire projetee : 37.89 m2

Z local : -0.14 a +0.17 m

Origine : P00 du PDF, non localisee sur site



Nord non documente

Cote	XY (m)	Z debut / fin (m)
C01	0.84	+0.00 / -0.00
C02	0.67	-0.00 / -0.00
C03	3.55	-0.00 / +0.04
C04	0.53	+0.04 / +0.03
C05	2.82	+0.03 / -0.02
C06	2.59	-0.02 / -0.08
C07	0.46	-0.08 / -0.10
C08	2.15	-0.10 / +0.17
C09	4.92	+0.17 / +0.03
C10	2.32	+0.03 / -0.09
C11	1.44	-0.09 / -0.14
C12	1.15	-0.14 / -0.12
C13	0.12	-0.12 / -0.14
C14	0.76	-0.14 / -0.05
C15	1.62	-0.05 / -0.03
C16	0.91	-0.03 / -0.08
C17	0.50	-0.08 / -0.07
C18	1.50	-0.07 / -0.04
C19	0.51	-0.04 / -0.02
C20	0.93	-0.02 / +0.05
C21	0.00	+0.05 / +0.05
C22	1.63	+0.05 / +0.00
C23	2.60	+0.00 / +0.00

XY deduits du trace vectoriel calibre.

Z cotes dans le PDF, arrondis au cm.

Aucun assemblage physique valide.

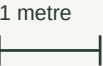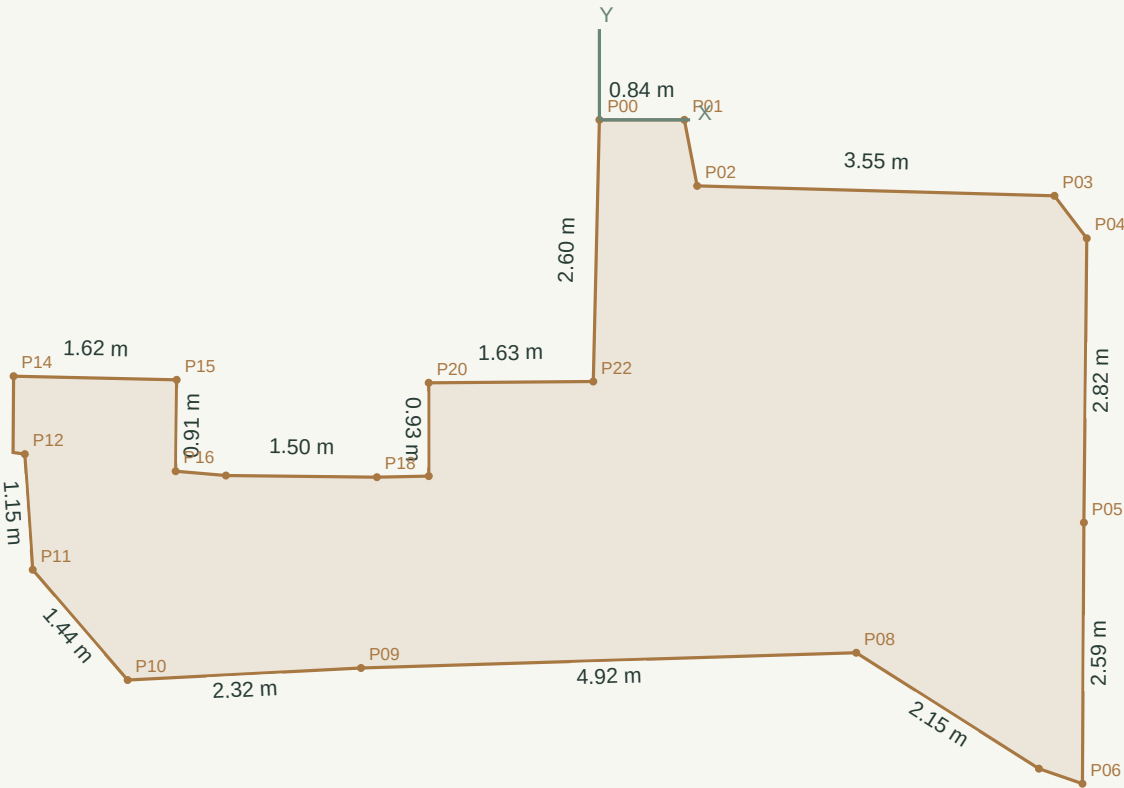


A3 paysage - 1:75 a 100 %, sans adaptation a la page

Source : Terrasse de droite.pdf, p.1-2. Tableau : valeurs publiees. Dessin : reconstruction vectorielle.

Ce document est une base partielle de restitution, pas un plan d implantation, de propriete ou d execution.

Terrasse de gauche

BASE DE CONTROLE - Releve independant, non raccorde au site

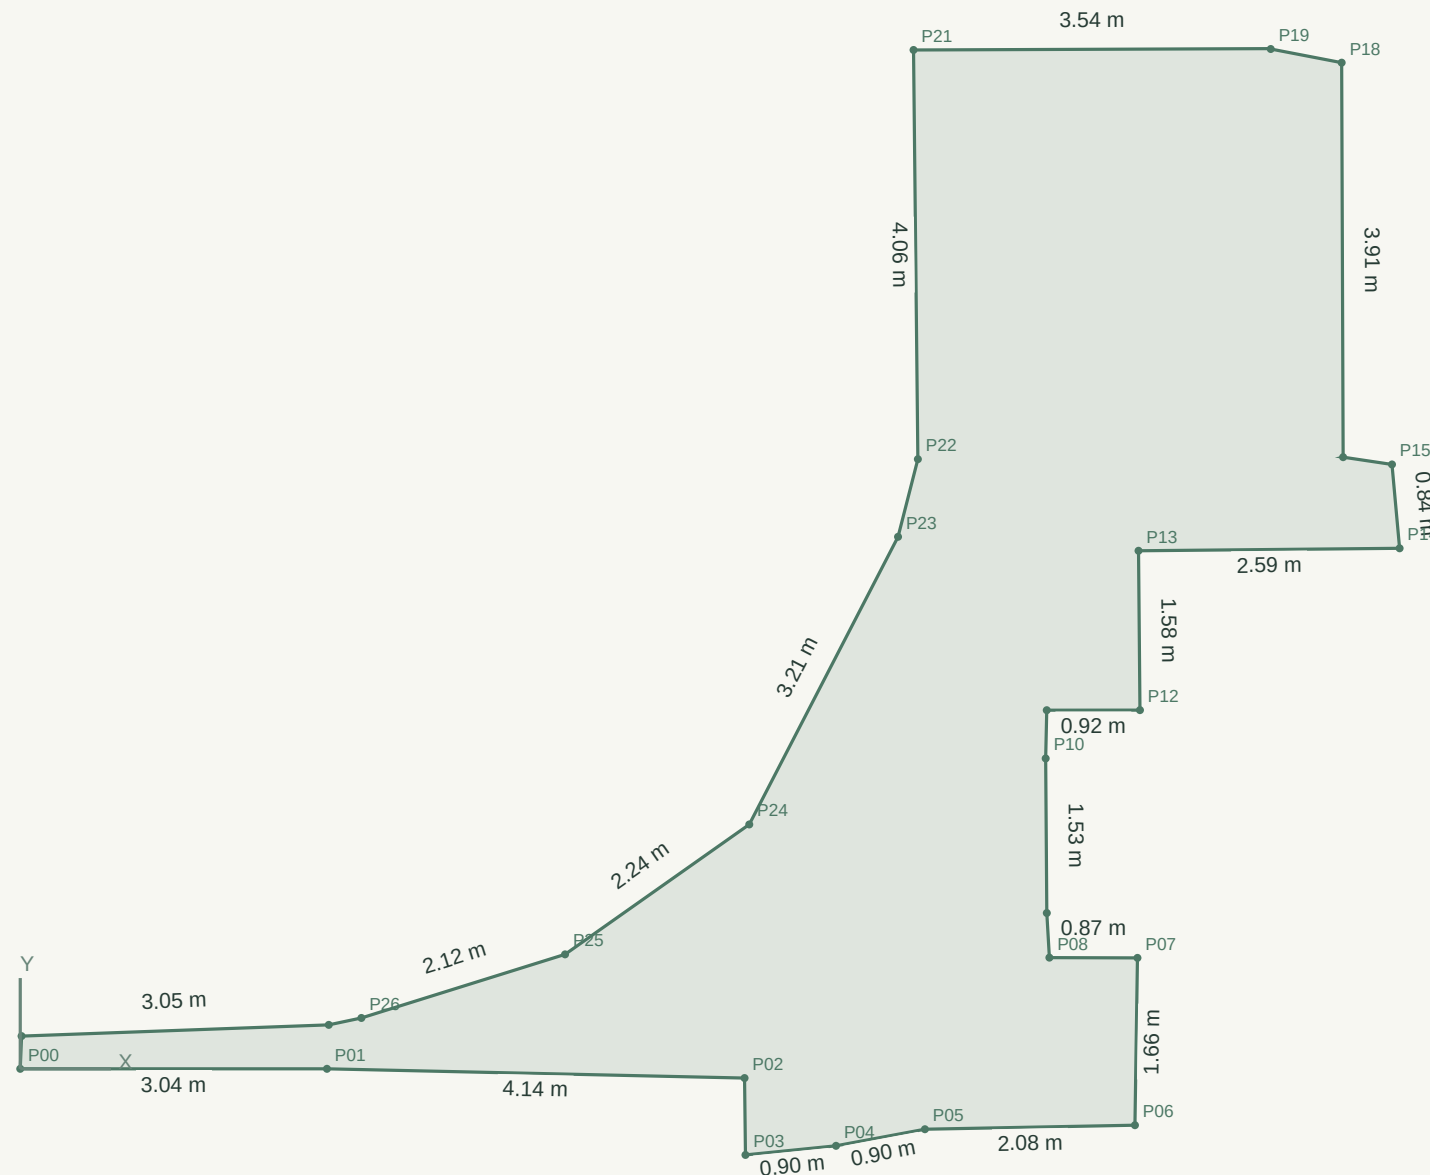

DONNEES LOCALES

Unites : metres | Geometrie : 1:1

Parcours XY : 47.54 m

Aire projetee : 46.18 m2

Z local : -0.68 a +0.04 m

Origine : P00 du PDF, non localisee sur site

Nord non documente

Cote	XY (m)	Z debut / fin (m)
C01	3.04	+0.00 / -0.07
C02	4.14	-0.07 / -0.17
C03	0.76	-0.17 / -0.17
C04	0.90	-0.17 / -0.32
C05	0.90	-0.32 / -0.33
C06	2.08	-0.33 / -0.41
C07	1.66	-0.41 / -0.40
C08	0.87	-0.40 / -0.43
C09	0.44	-0.43 / -0.45
C10	1.53	-0.45 / -0.48
C11	0.48	-0.48 / -0.48
C12	0.92	-0.48 / -0.51
C13	1.58	-0.51 / -0.51
C14	2.59	-0.51 / -0.58
C15	0.84	-0.58 / -0.60
C16	0.49	-0.60 / -0.59
C17	0.00	-0.59 / -0.59
C18	3.91	-0.59 / -0.56
C19	0.72	-0.56 / -0.61
C20	0.00	-0.61 / -0.61
C21	3.54	-0.61 / -0.60
C22	4.06	-0.60 / -0.66
C23	0.79	-0.66 / -0.68
C24	3.21	-0.68 / +0.02
C25	2.24	+0.02 / +0.00
C26	2.12	+0.00 / +0.04
C27	0.33	+0.04 / +0.03
C28	3.05	+0.03 / +0.02
C29	0.32	+0.02 / +0.00

XY deduits du trace vectoriel calibre.

Z cotes dans le PDF, arrondis au cm.

Aucun assemblage physique valide.

1 metre

A horizontal line with vertical end caps, representing a scale bar for 1 metre.

A3 paysage - 1:75 a 100 %, sans adaptation a la page

Source : Terrasse de gauche.pdf, p.1-2. Tableau : valeurs publiees. Dessin : reconstruction vectorielle.

Ce document est une base partielle de restitution, pas un plan d implantation, de propriete ou d execution.

Zone escalier

BASE DE CONTROLE - Releve independant, non raccorde au site

DONNEES LOCALES

Unites : metres | Geometrie : 1:1

Parcours XY : 15.68 m



Aire projetee : 8.59 m2

Z local : -0.62 a +0.92 m

Origine : P00 du PDF, non localisee sur site

Nord non documente

Cote	XY (m)	Z debut / fin (m)
C01	1.20	+0.00 / -0.19
C02	1.22	-0.19 / -0.41
C03	0.08	-0.41 / -0.56
C04	2.37	-0.56 / -0.62
C05	0.46	-0.62 / -0.55
C06	0.11	-0.55 / -0.02
C07	1.03	-0.02 / +0.15
C08	0.71	+0.15 / +0.24
C09	0.03	+0.24 / +0.18
C10	2.40	+0.18 / +0.17
C11	1.47	+0.17 / +0.23
C12	0.73	+0.23 / +0.35
C13	0.18	+0.35 / +0.47
C14	1.11	+0.47 / +0.55
C15	0.13	+0.55 / +0.70
C16	1.08	+0.70 / +0.79
C17	0.10	+0.79 / +0.92
C18	1.01	+0.92 / +0.89
C19	0.27	+0.89 / +0.00

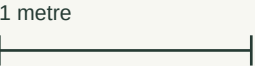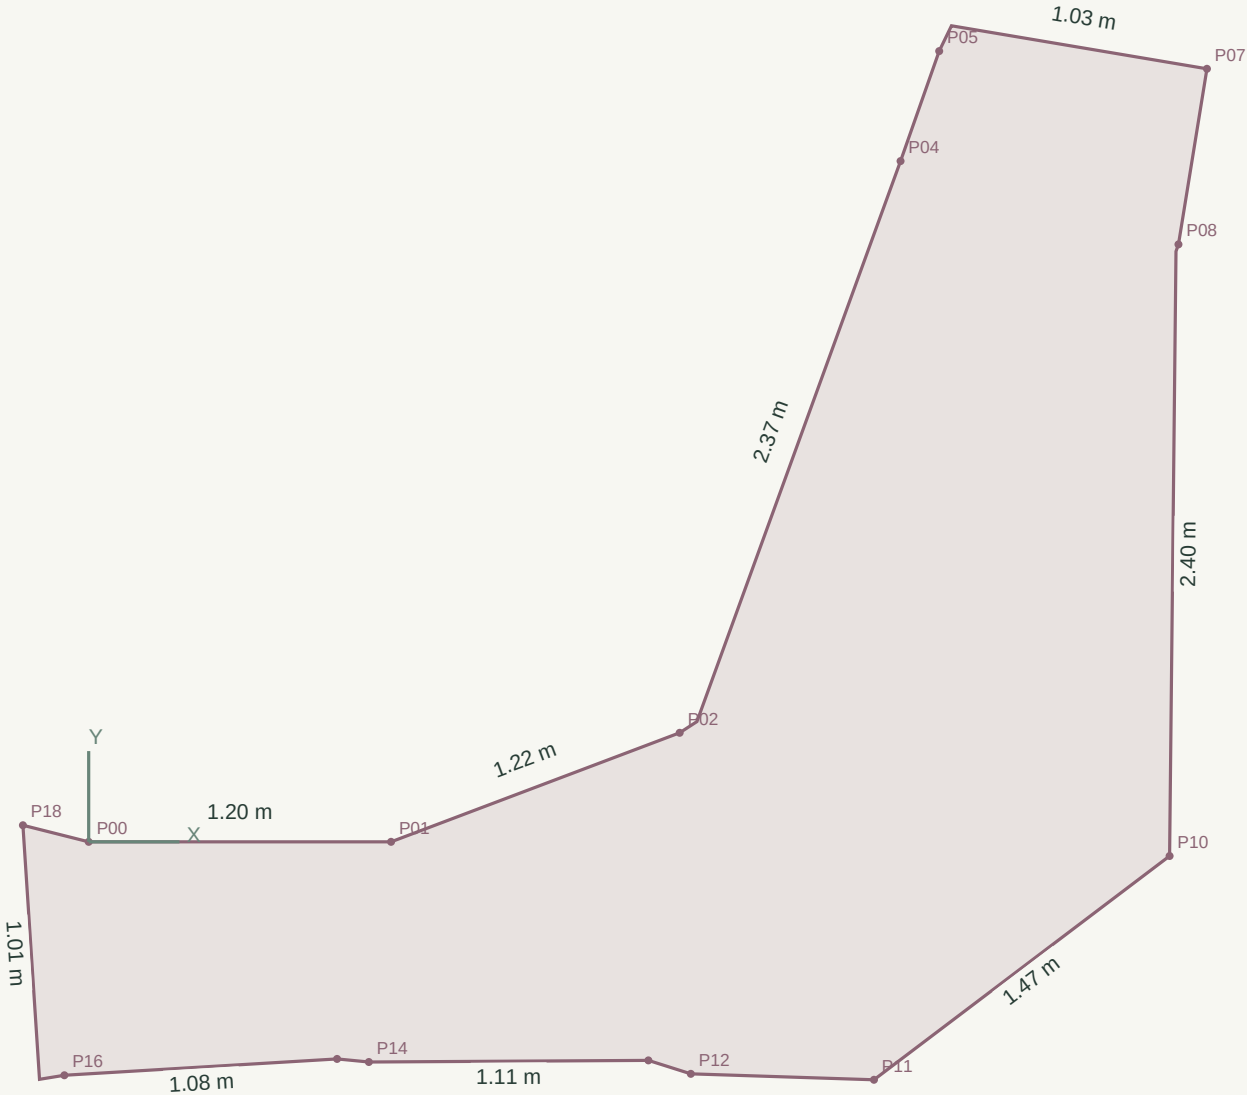

A3 paysage - 1:30 a 100 %, sans adaptation a la page

Source : Zone escalier.pdf, p.1-2. Tableau : valeurs publiees. Dessin : reconstruction vectorielle.

Ce document est une base partielle de restitution, pas un plan d implantation, de propriete ou d execution.

XY deduits du trace vectoriel calibre.

Z cotes dans le PDF, arrondis au cm.

Aucun assemblage physique valide.